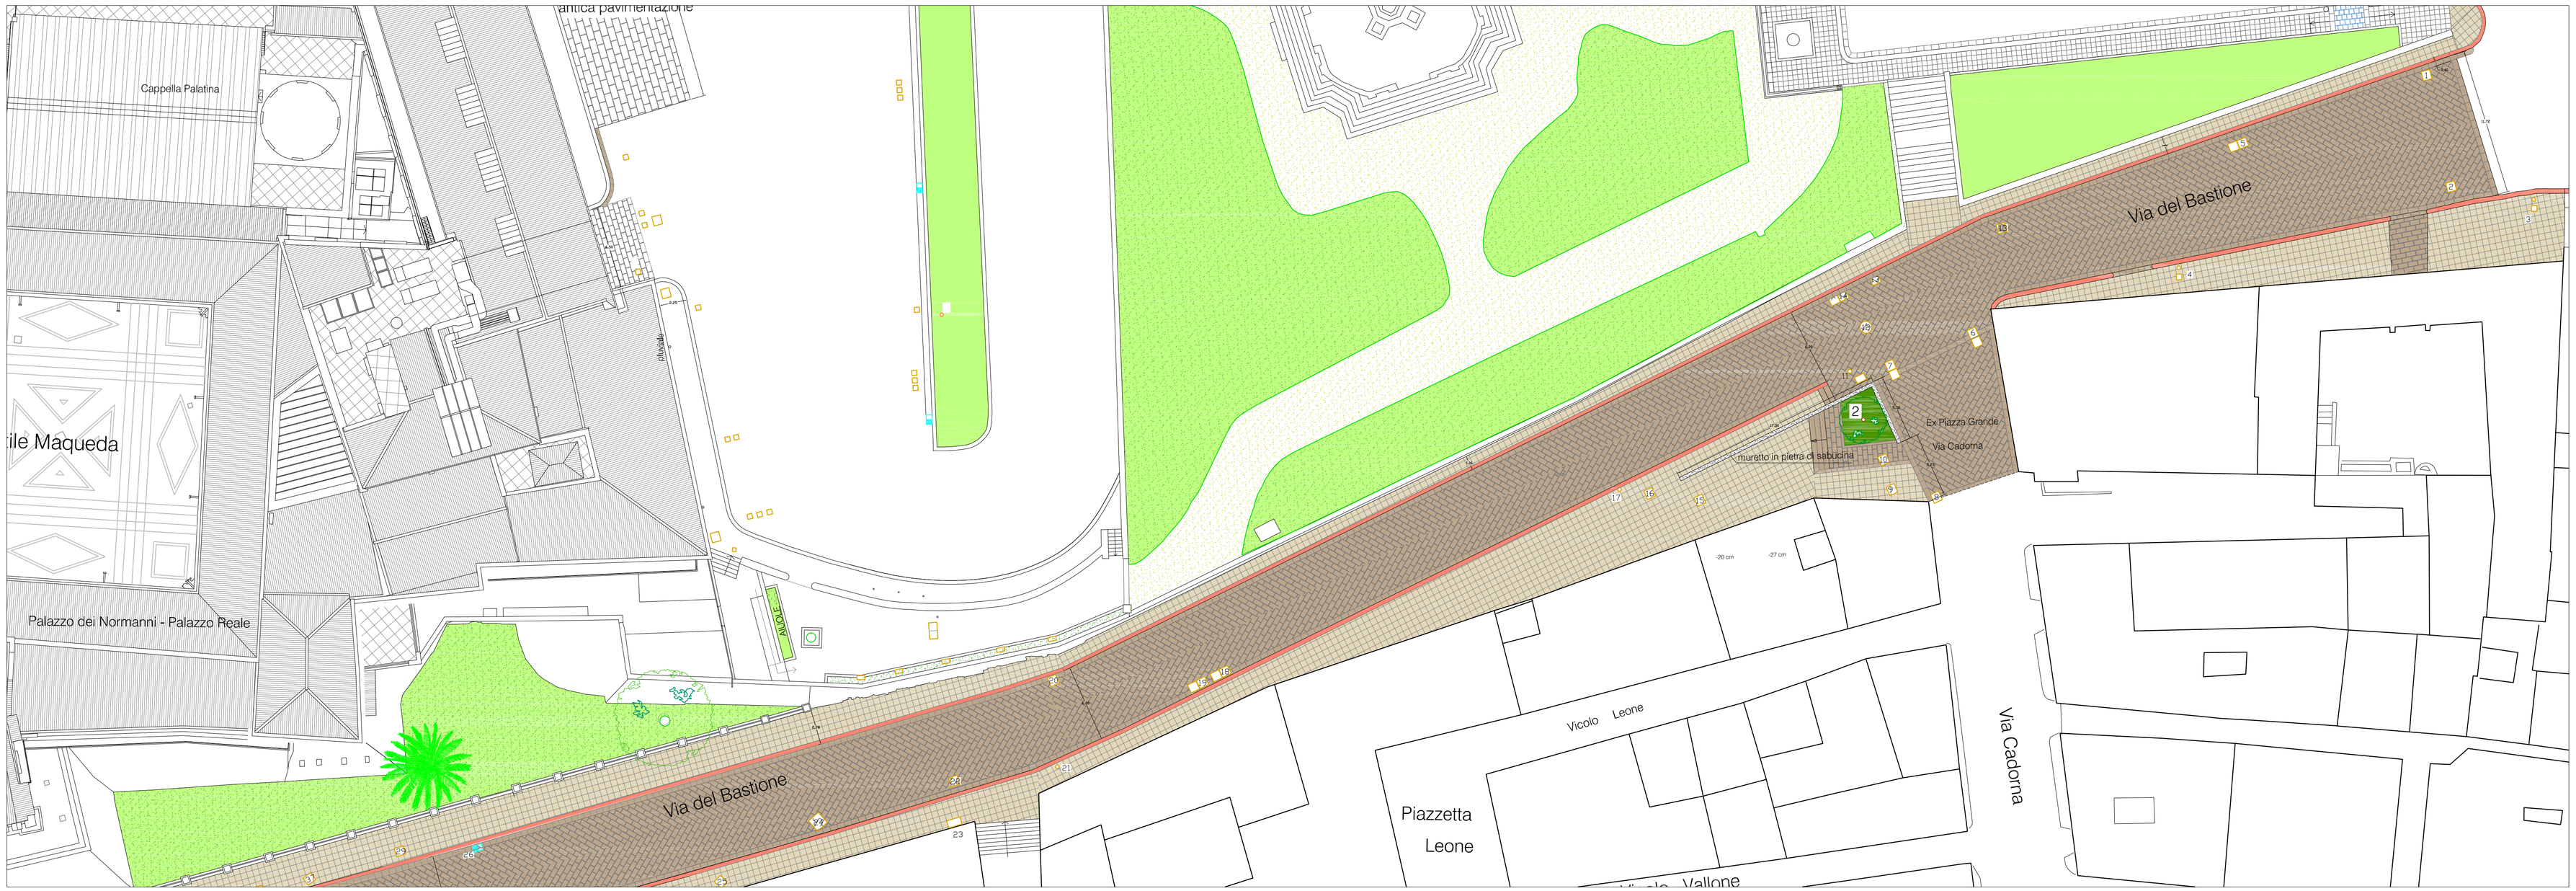

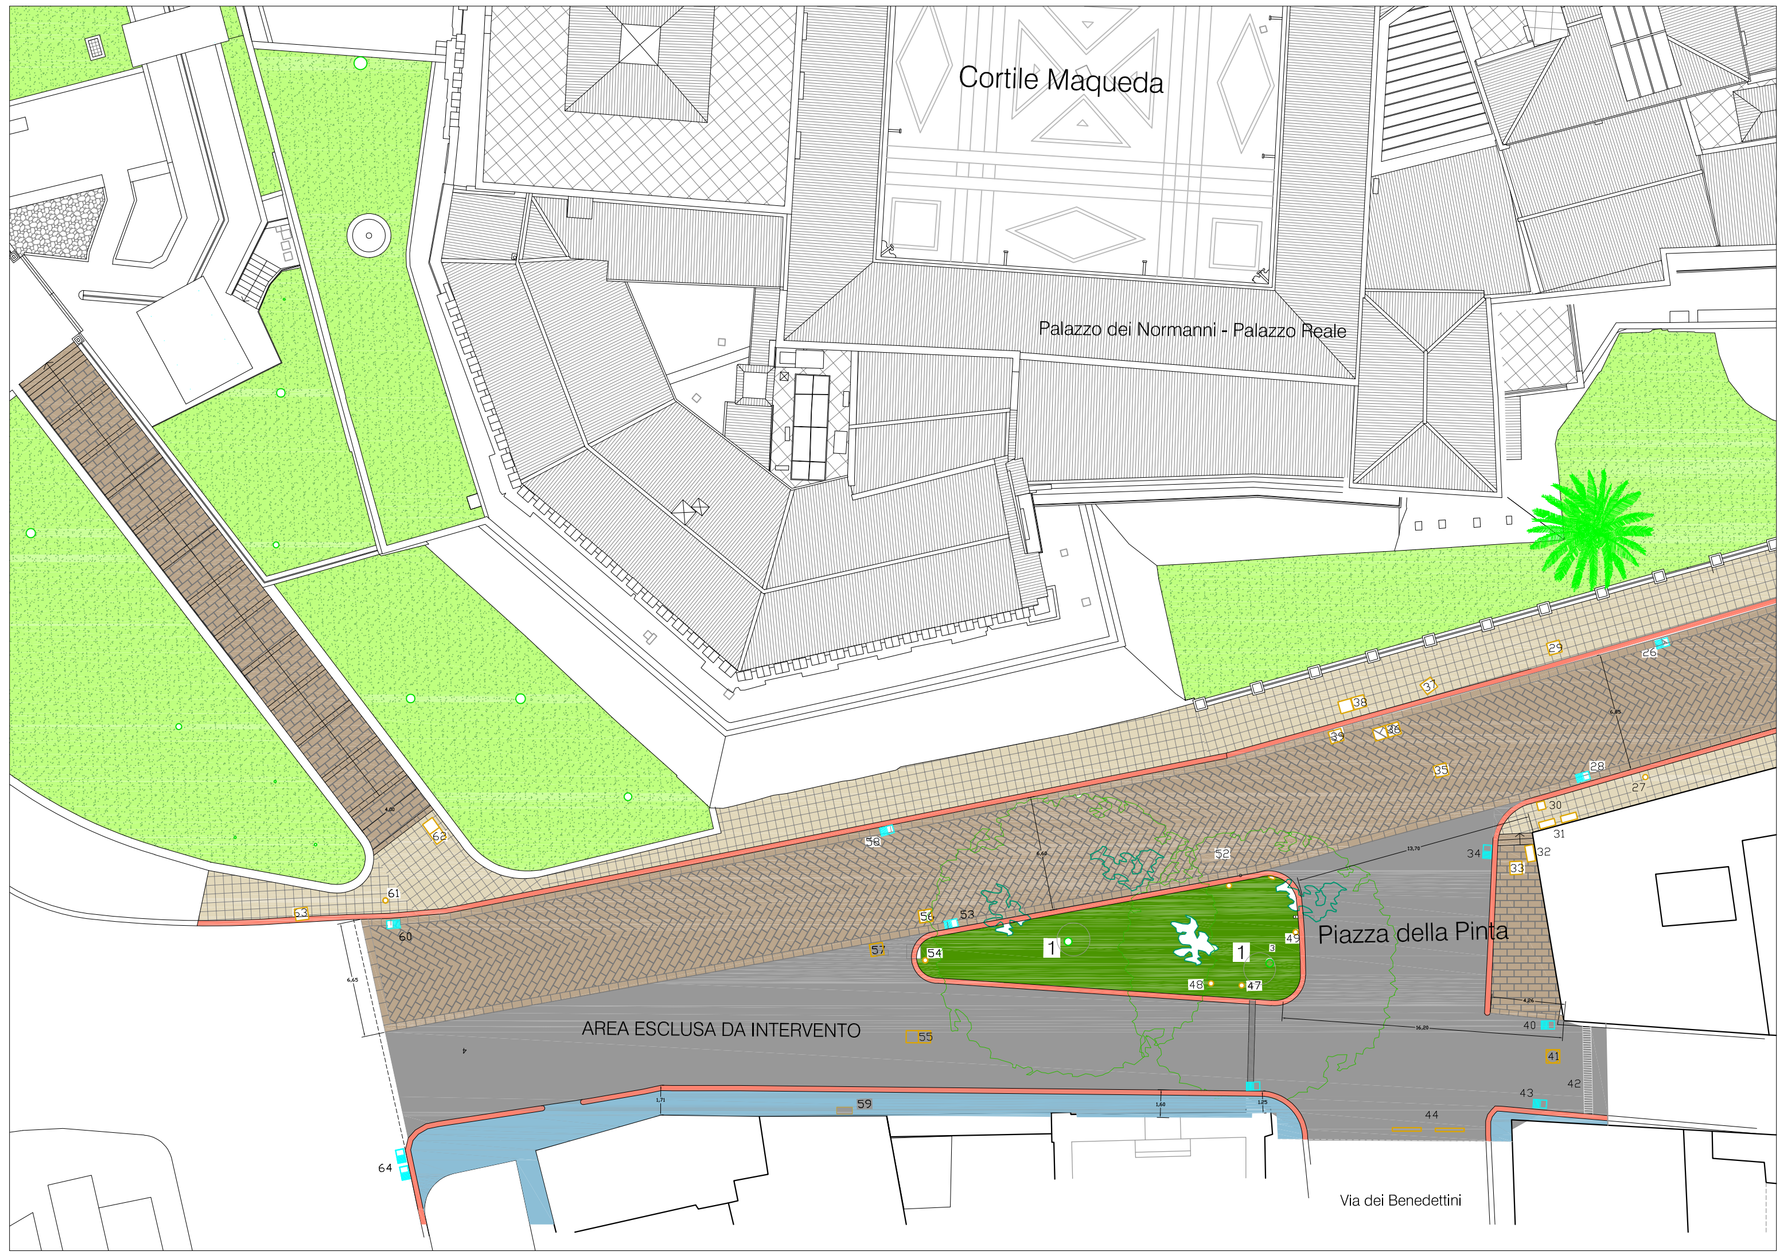

LEGENDA IMPIANTISTICA SEDE STRADALE E MARCIAPIEDI:

1 Pozzetto Siptel
2 Pozzetto Siptel
3 Palo Pastorale e pozzetto AMG
4 Palo Pastorale e pozzetto AMG
5 Pozzetto Fast Web
6 Pozzetto Siptel
7 Pozzetto open fiber
8 Pozzetto Fast Web
9 Pozzetto fognatura AMAP
10 Pozzetto Siptel
11 Palo illuminazione AMG
12 Pozzetti idrico AMAP
13 Pozzetti Siptel
14 Pozzetto Fast Web
15 Pozzetto fognatura AMAP
16 Pozzetto open fiber
17 Palo illuminazione AMG
18 Pozzetto ENEL
19 Pozzetto ENEL
20 Pozzetto Siptel
21 Palo illuminazione AMG
22 Pozzetto open fiber
23 Armadio stradale ENEL
24 Pozzetto altro
25 Pozzetto fognatura AMAP
26 Caditoia AMAP 80X50
27 Palo illuminazione AMG
28 Caditoia AMAP 80X50
29 Pozzetto Siptel
30 Pozzetto P.I. AMG 40x40
31 Armadio stradale ENEL
32 Armadio stradale ENEL
33 Pozzetto Fast Web
34 Caditoia AMAP 80X50
35 Pozzetto Siptel
36 Pozzetto Fast Web
37 Pozzetto Siptel
38 Pozzetto Fast Web
39 Pozzetto Siptel
40 Caditoia AMAP 80X50
41 Pozzetto fognatura AMAP
42 Griglia di raccolta acque piovane
43 Caditoia AMAP 80X50
44 Barriere tipo Parigi
45 Caditoia AMAP 80X50
46 Griglia di raccolta acque piovane
47 Palo illuminazione AMG
48 Palo con telecamere videosorveglianza
49 Palo illuminazione AMG
50 Presa idrante AMAP
51 Palo illuminazione AMG
52 Caditoia AMAP 80X50
53 Caditoia AMAP 80X50
54 Palo illuminazione AMG
55 Pozzetto open fiber
56 Pozzetto fognatura AMAP
57 Pozzetto fognatura AMAP
58 Caditoia AMAP 80X50
59 Armadio stradale ENEL
60 Caditoia AMAP 80X50
61 Palo illuminazione AMG
62 Pozzetto Siptel
63 Pozzetto fognatura AMAP
64 Caditoie AMAP 80X50

LEGENDA MAPPATURA DELLE PAVIMENTAZIONI:

- Orlatura di marciapiedi in pietra calcarea con sezione retta
- Pavimentazione marciapiedi in basole quadre
- Pavimentazione in basole di pietra di Billiemi e mista
- Gradini in pietra tipo Billiemi
- zona non oggetto d'intervento
- muretto/seduta h.cm 40 in pietra di sabucina
- Pavimentazione di marciapiedi in battuto cementizio

LEGENDA BOTANICA: 1. Ficus Microcarpa 2. Jacaranda

COMUNE DI PALERMO
Area Urbanistica e della Rigenerazione Urbana,
della Mobilità e del Centro Storico
Settore Rigenerazione Urbana e del Centro Storico

CONTRATTO ISTITUZIONALE DI SVILUPPO (CIS) *"PALERMO - CENTRO STORICO"*
PIANO OPERATIVO "CULTURA E TURISMO" - FSC 2014/2020

INTERVENTI DI RIQUALIFICAZIONE URBANA DELLE PAVIMENTAZIONI STORICHE E DEGLI SPAZI APERTI NEL CENTRO STORICO DI PALERMO - ACCORDO QUADRO

Coordinatori della Progettazione:
Arch. Salvatore Giardina
Arch. Giuseppe Prestigiacomo

Gruppo di Progettazione:
Ing. Edoardo Intravaia
Arch. Stefano Gueli
Arch. Angela Gebbia
Arch. Fabrizio Ferro
Geom. Giovanni Castronovo
Geom. Gioacchino Manzella
Geom. Eugenio Butera
Geom. Giuseppe Carroccetto

Coordinatore per la sicurezza
Arch. Gianfranco Geraci

Intervento:
LAVORI DI MANUTENZIONE STRAORDINARIA DELLE PAVIMENTAZIONI DI VIA DEL BASTIONE E PIAZZA DELLA PINTA

LOTTO N.12

CONTRATTO APPLICATIVO - AMBITO "C" PIEDE FENICIO

Elaborato:
PROGETTO DELLE PAVIMENTAZIONI, MAPPATURA DEI MATERIALI, SCHEMI TIPOLOGICI E IMPIANTISTICA SEDE STRADALE

Data: Giugno 2023

Elab.
TAV.8

SCALA 1:250

Responsabile Unico del Procedimento
Ing. Michele Milano