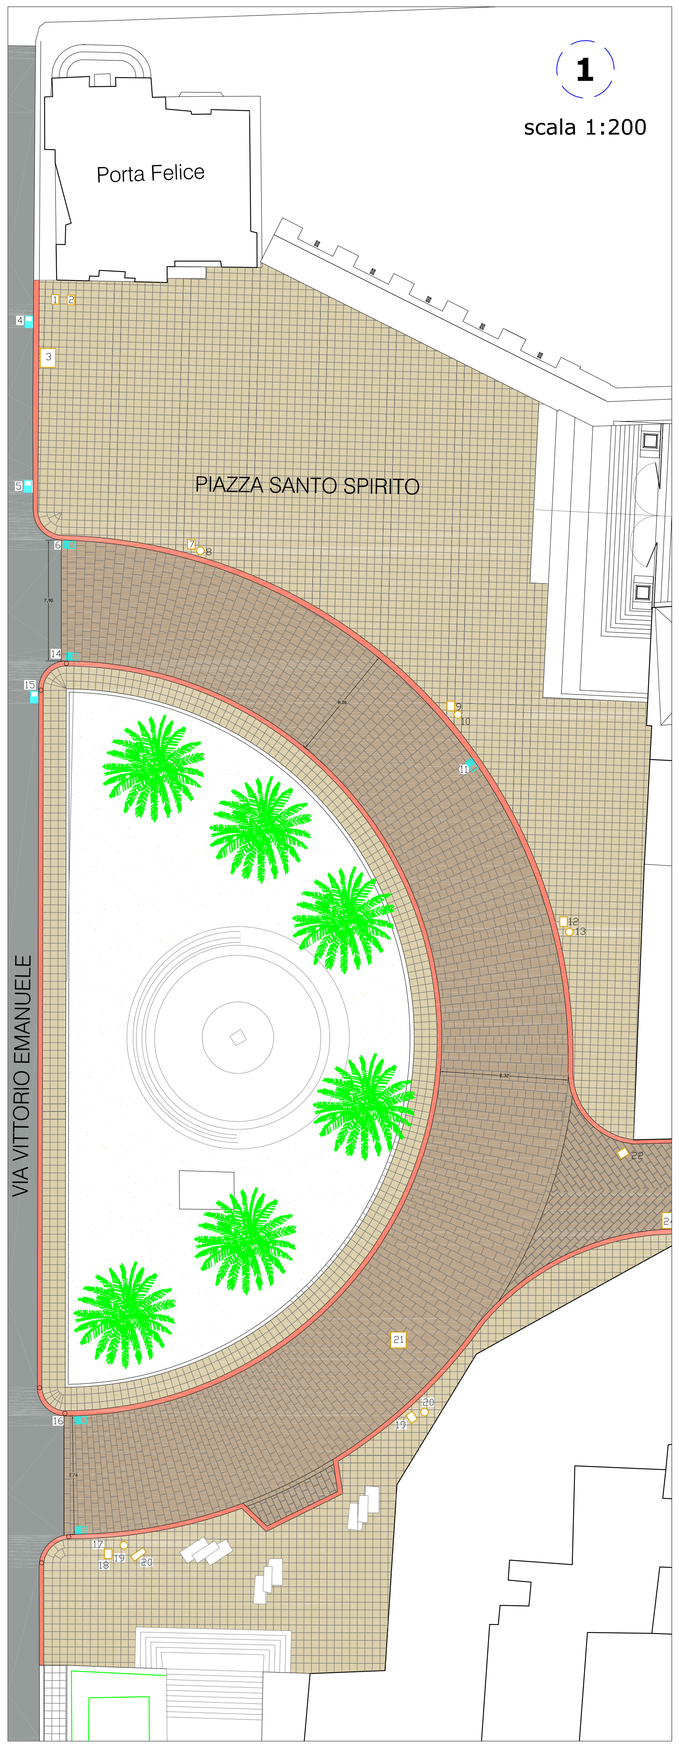

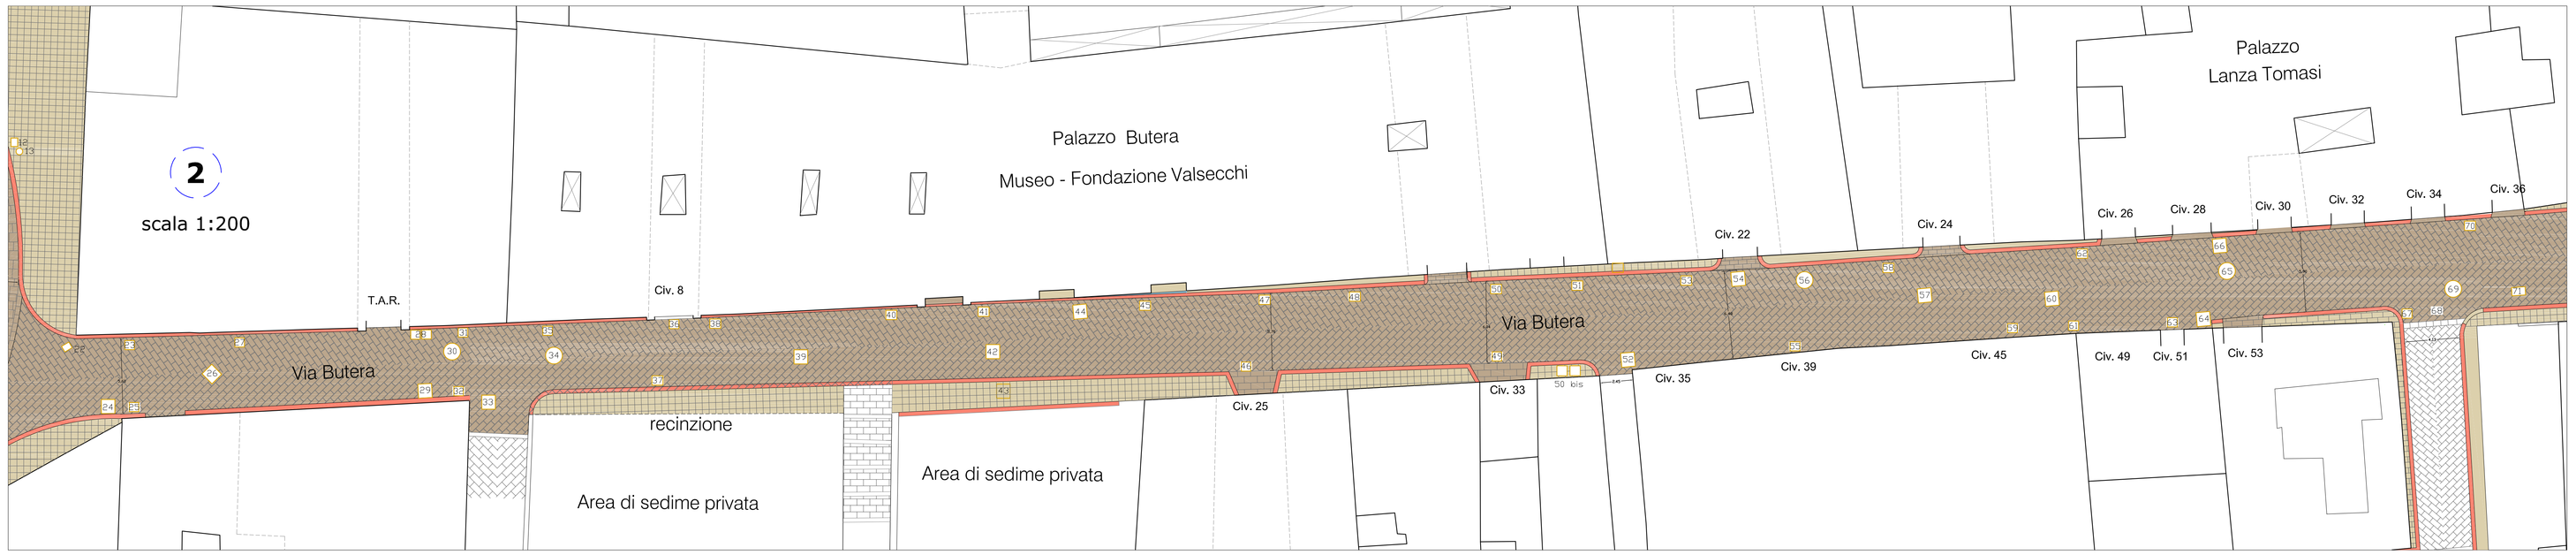

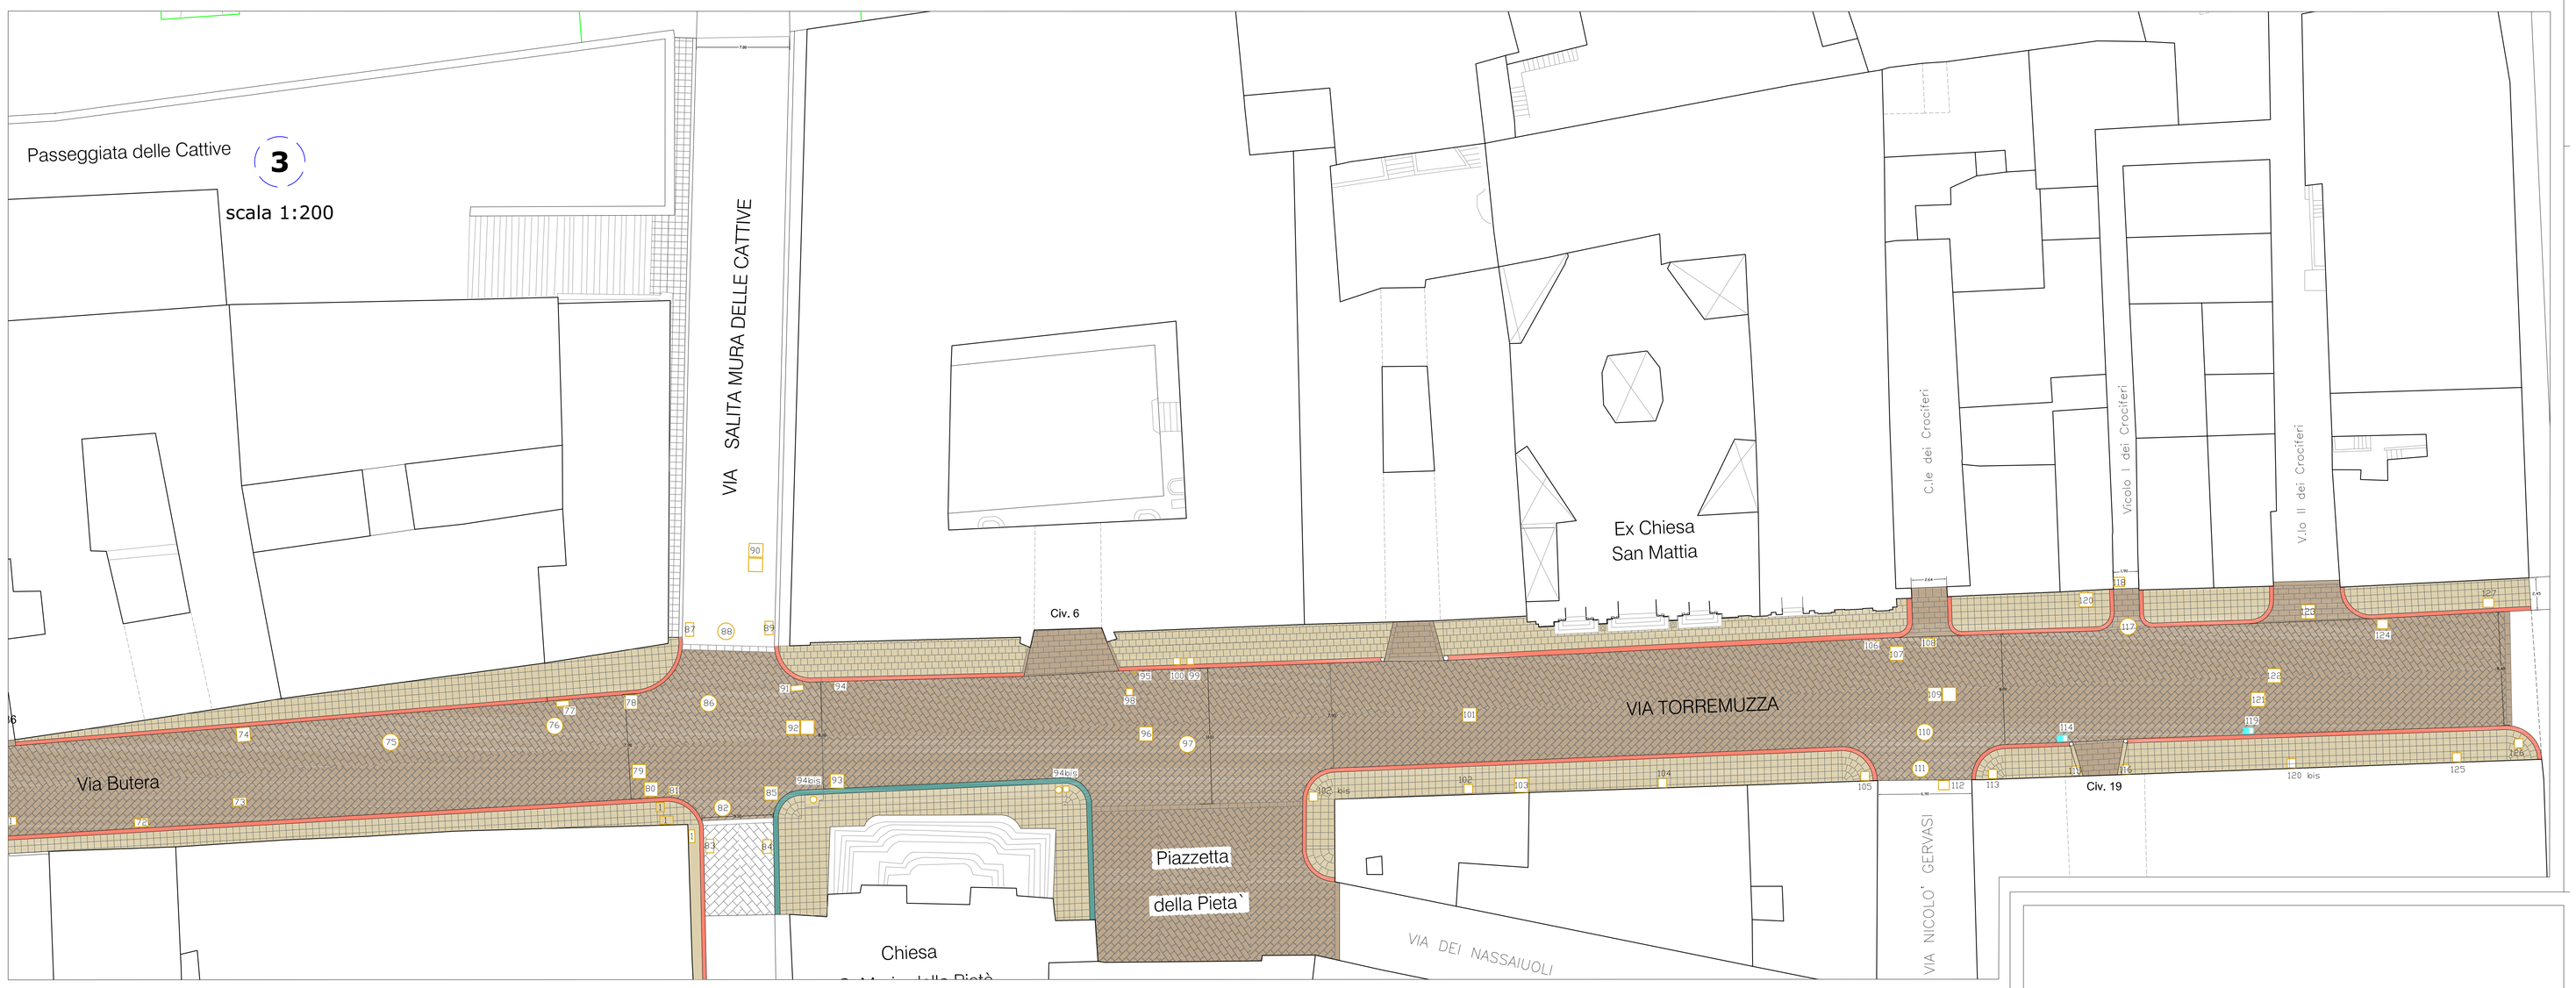

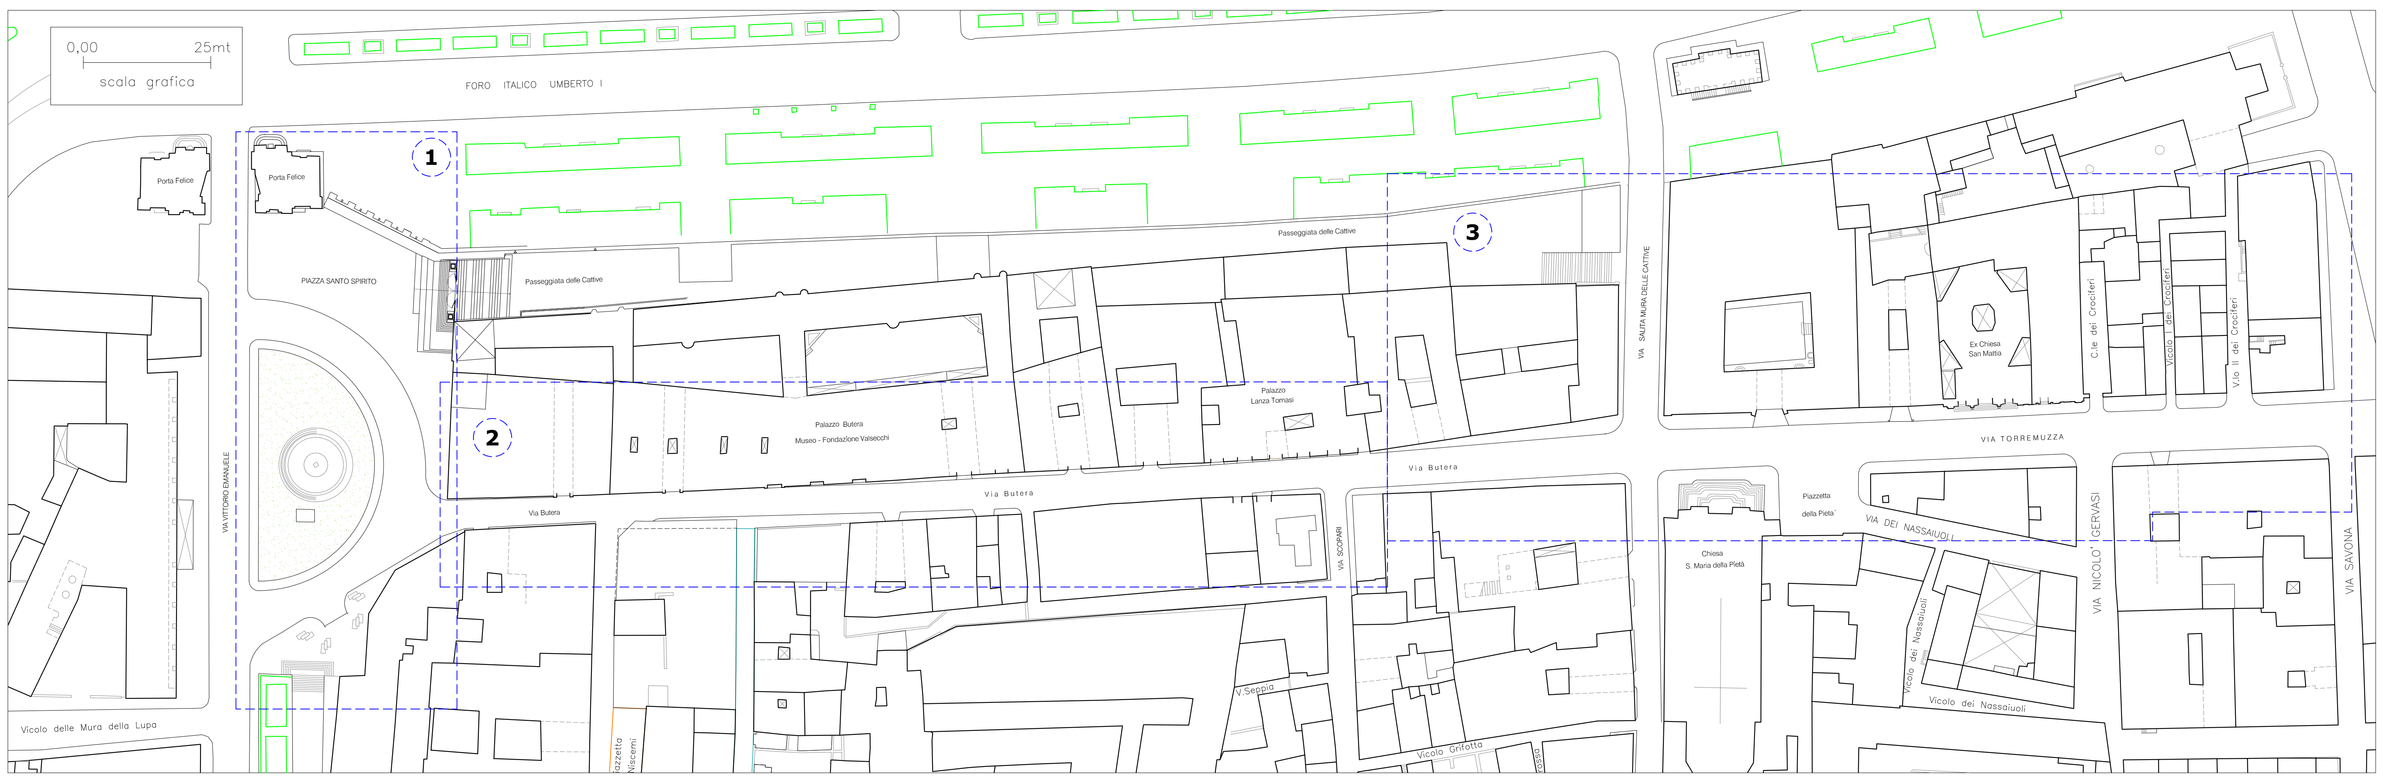

LEGENDA MAPPATURA DELLE PAVIMENTAZIONI

- Orlatura di marciapiedi in pietra di Billiemi con sezione a toro
- Orlatura di marciapiedi in pietra calcarea con sezione retta
- Pavimentazione di marciapiedi in basole di pietra calcarea grigia
- Pavimentazione stradale in basole di pietra calcarea grigia
- Pavimentazione stradale in basole di pietra calcarea grigia disposta a raggiera (Piazza Santo Spirito)

COMUNE DI PALERMO
Area Urbanistica e della Rigenerazione Urbana,
della Mobilità e del Centro Storico
Settore Rigenerazione Urbana e del Centro Storico

CONTRATTO ISTITUZIONALE DI SVILUPPO (CIS) *"PALERMO - CENTRO STORICO"*
PIANO OPERATIVO "CULTURA E TURISMO"- FSC 2014/2020

INTERVENTI DI RIQUALIFICAZIONE URBANA DELLE PAVIMENTAZIONI STORICHE E DEGLI SPAZI APERTI NEL CENTRO STORICO DI PALERMO - ACCORDO QUADRO

Coordinatori della Progettazione:
Arch. Salvatore Giardina
Arch. Giuseppe Prestigiacomo

Gruppo di Progettazione:
Ing. Edoardo Intravaia
Arch. Stefano Gueli
Arch. Angela Gebbia
Arch. Fabrizio Ferro
Geom. Giovanni Castronovo
Geom. Gioacchino Manzella
Geom. Eugenio Butera
Geom. Giuseppe Carrocetto

Coordinatore per la sicurezza
Arch. Gianfranco Geraci

Intervento:
LAVORI DI MANUTENZIONE STRAORDINARIA DELLE PAVIMENTAZIONI DI VIA BUTERA VIA TORREMUZZA E PIAZZA SANTO SPIRITO

LOTTO N.4

CONTRATTO APPLICATIVO - AMBITO "A" KALSA

Elaborato:
PROGETTO PAVIMENTAZIONI E MAPPATURA DEI MATERIALI E RILIEVO IMPIANTISTICA SEDE STRADALE E MARCIAPIEDE

Data: Giugno 2023

Elab. TAV.8

SCALA 1:200

Responsabile Unico del Procedimento
Ing. Michele Milano